
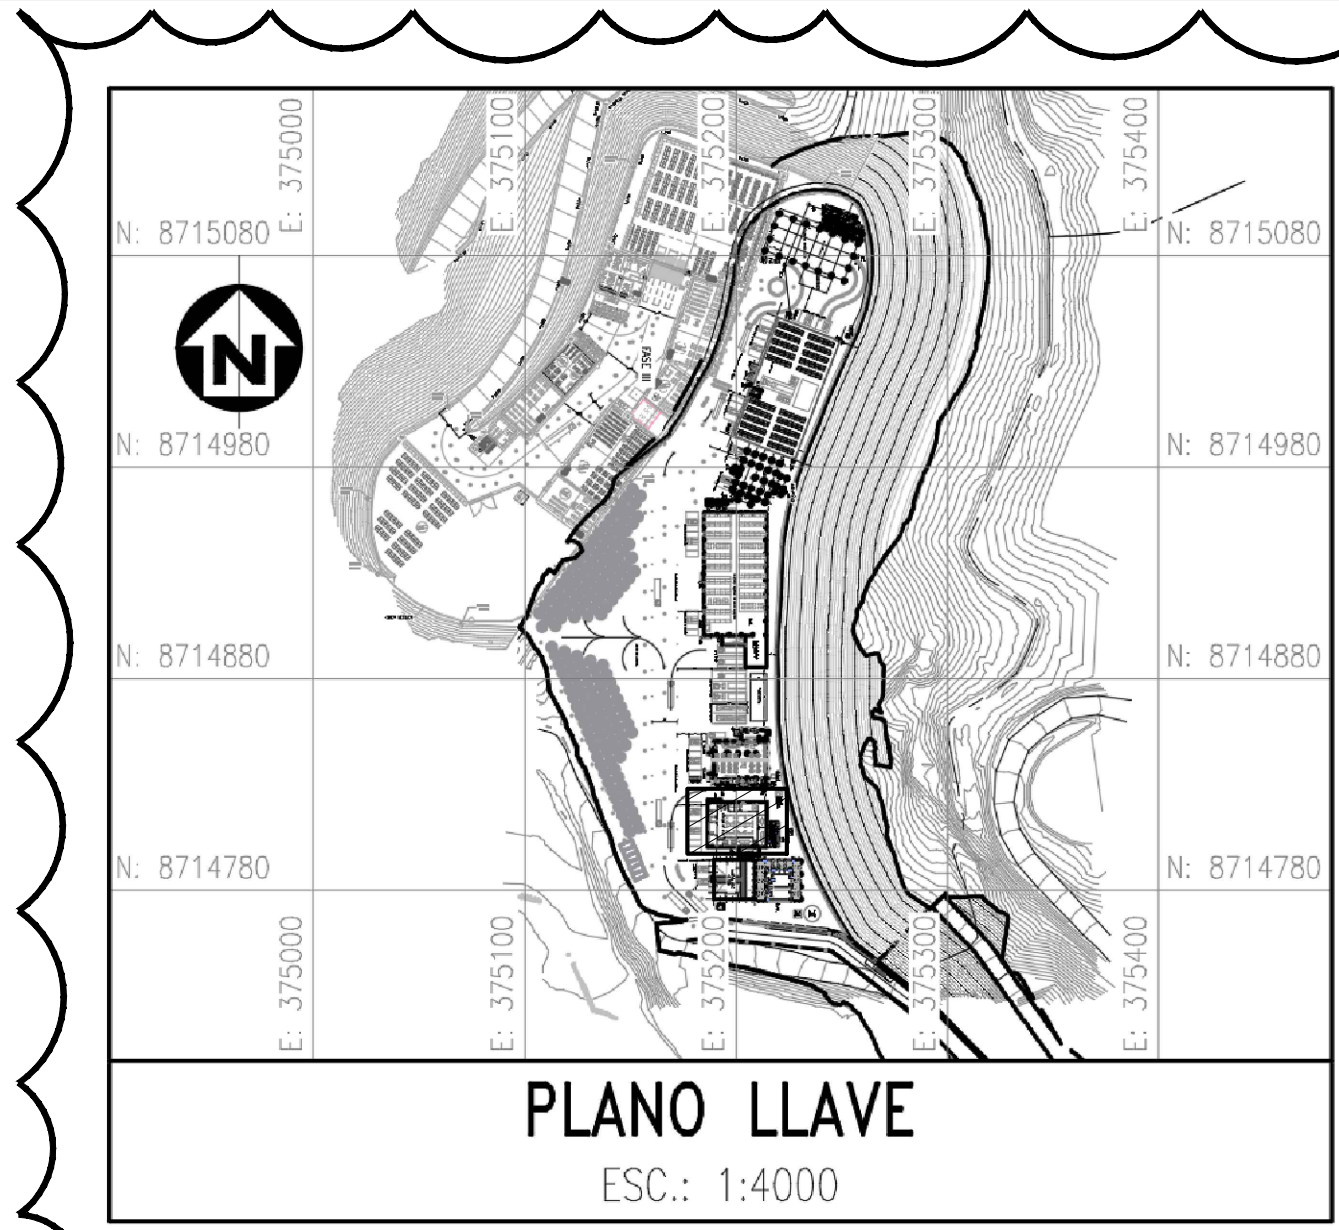
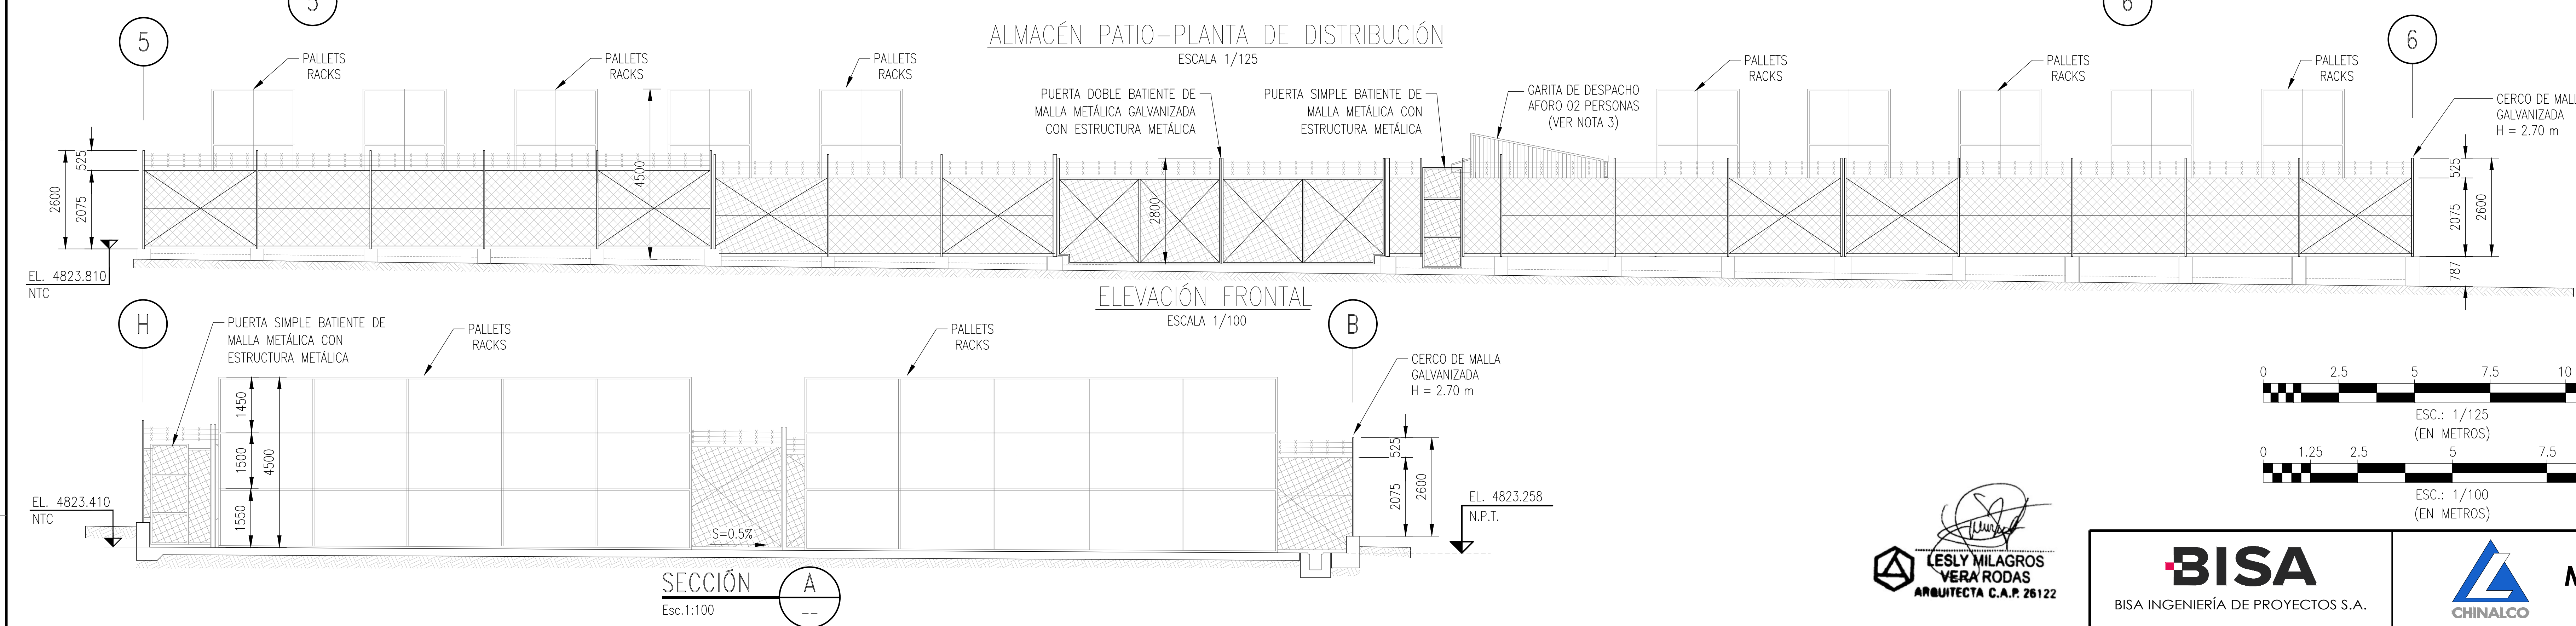


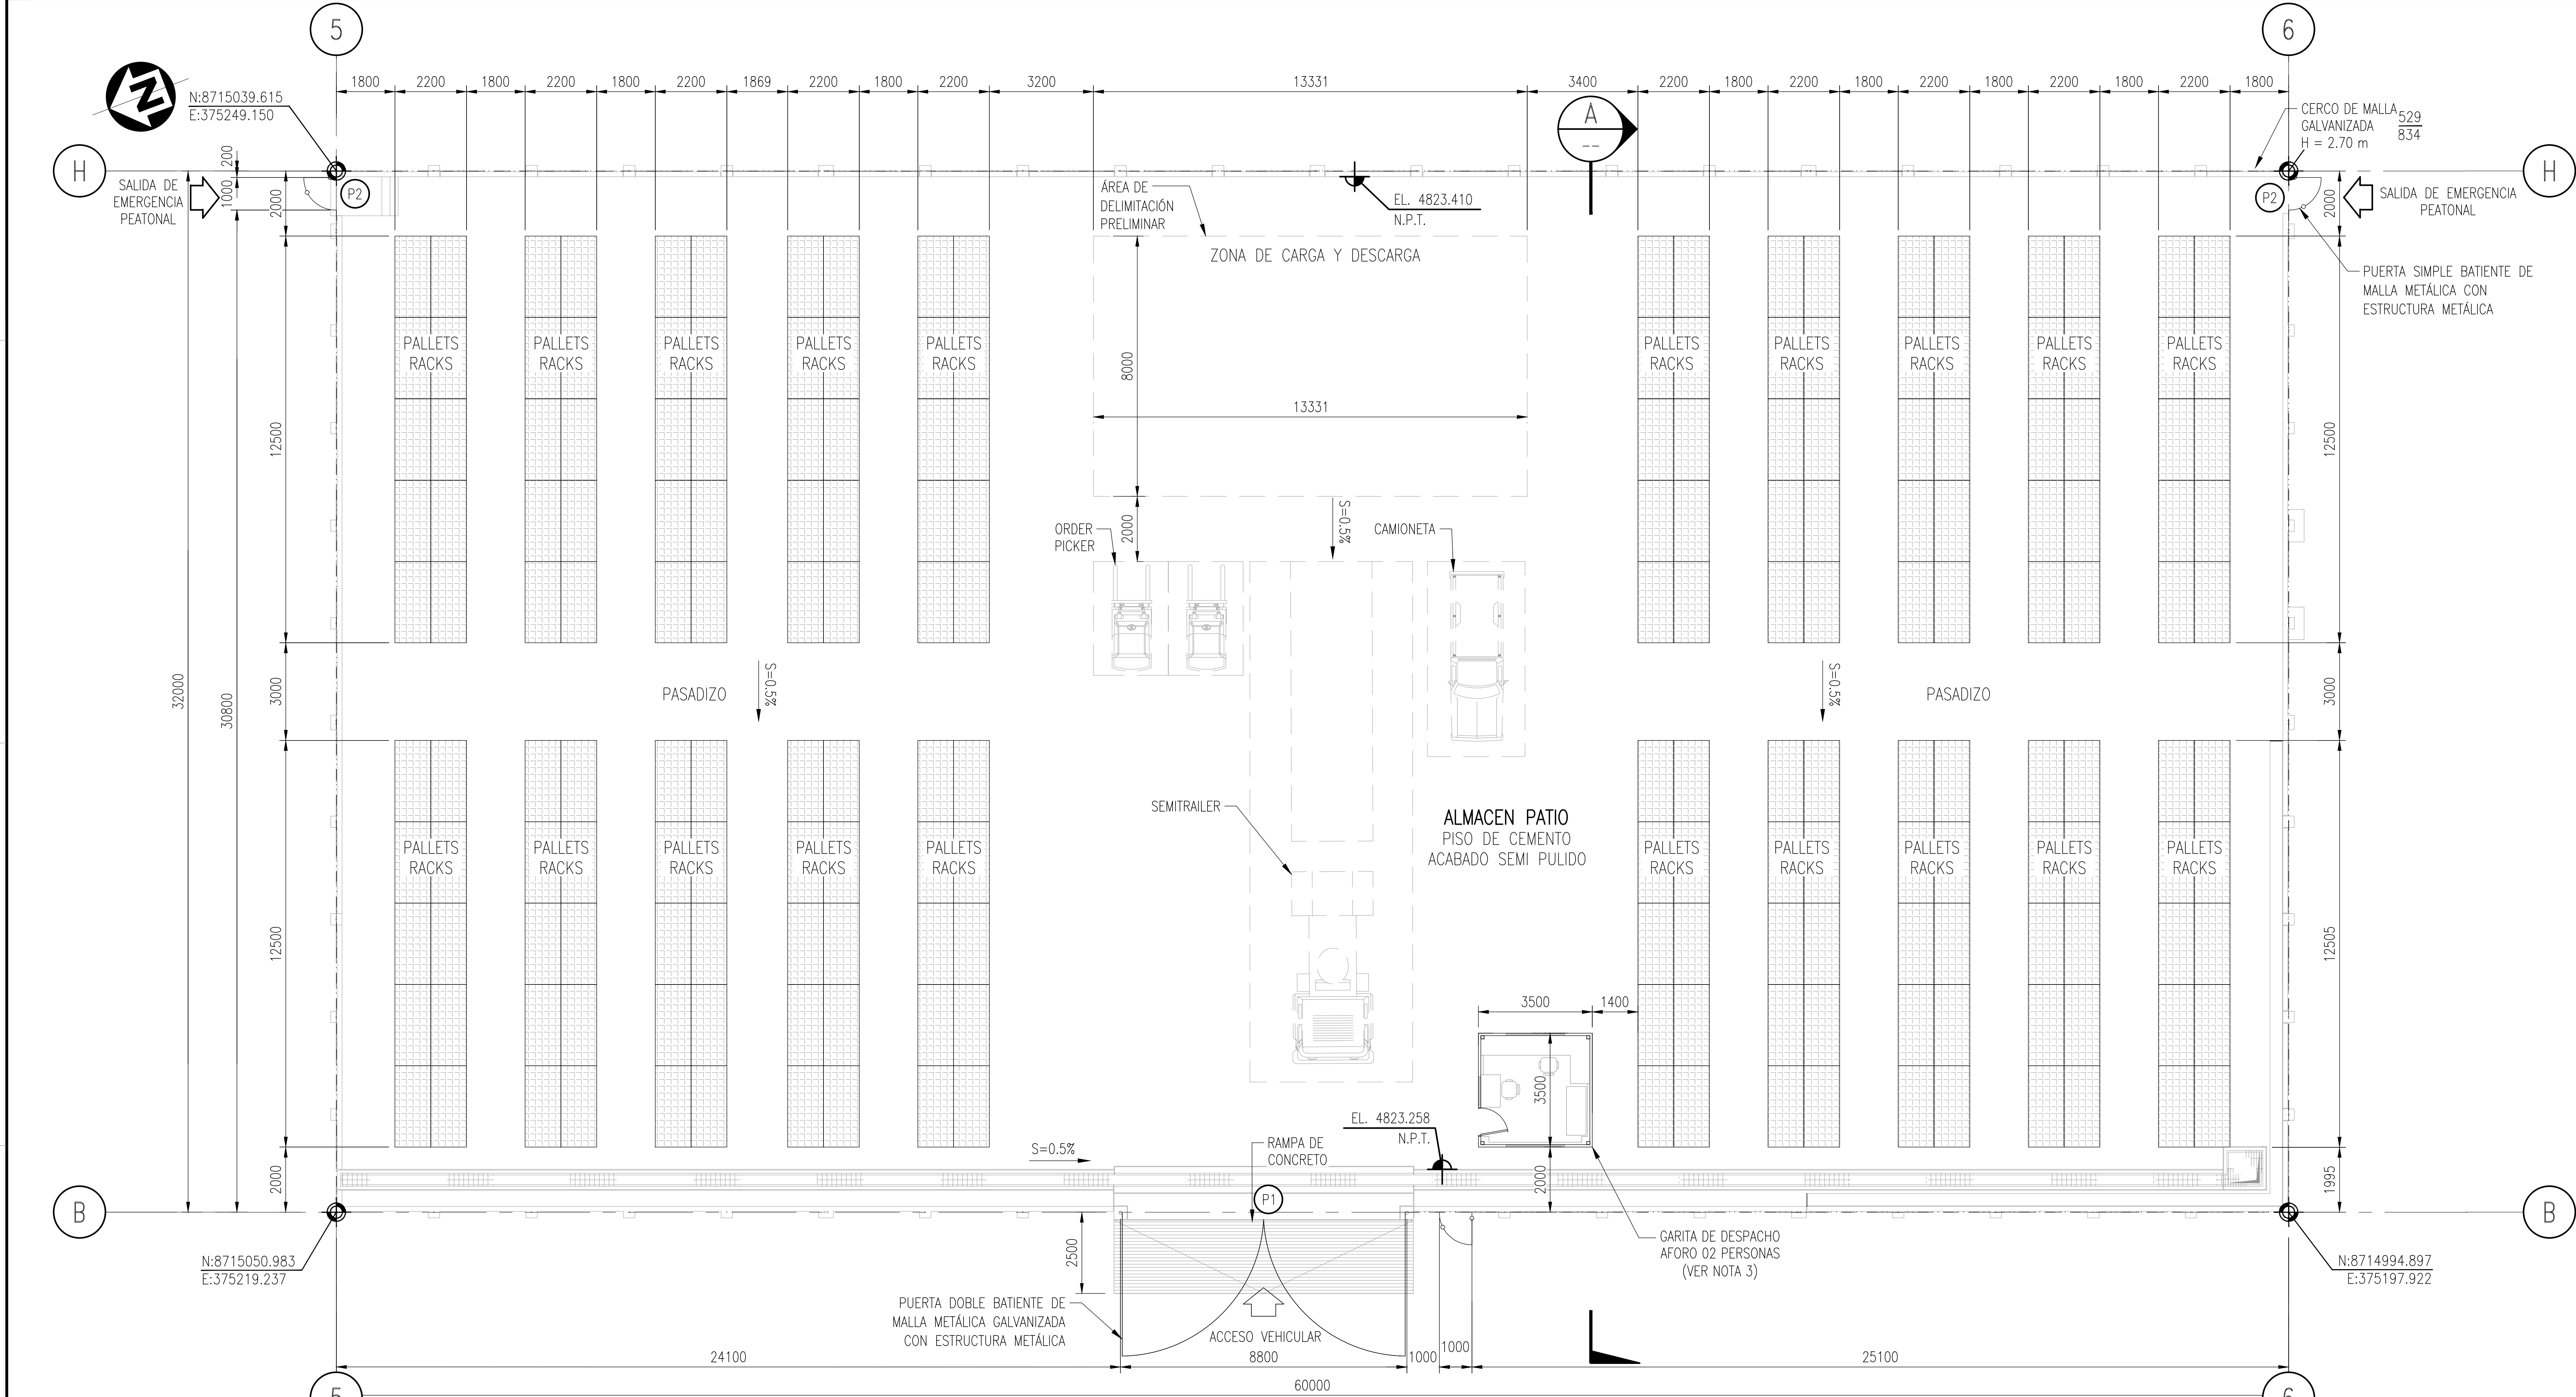


INFORMACIÓN DE LAS EDIFICACIONES				
ÍTEM	COMPONENTE	CANTIDAD	ÁREA TOTAL (m ²)	AFORO
1	ALMACÉN PATIO LOGÍSTICA	1	1920	07 PERS.

CUADRO DE VANOS – PUERTAS						
ÍTEM	SÍMBOLO	ANCHO	ALTO	CANTIDAD	UBICACIÓN	DESCRIPCIÓN
1	(P1)	8.80 m	2.80 m	1	ALMACÉN PATIO LOGÍSTICA	PUERTA DOBLE BATIENTE DE MALLA METÁLICA CON ESTRUCTURA METÁLICA
2	(P2)	1.00 m	2.00 m	2	ALMACÉN PATIO LOGÍSTICA	PUERTA SIMPLE BATIENTE DE MALLA METÁLICA CON ESTRUCTURA METÁLICA

LEYENDA	
SÍMBOLO	DESCRIPCIÓN
(A)	DESIGNACIÓN DE EJES
(1)	DESIGNACIÓN DE EJES
EL xxxx	SIMBOLOGÍA DE NIVEL PLANTA
EL xxxx	SIMBOLOGÍA DE NIVEL ELEVACIÓN
X	SIMBOLOGÍA DE SECCIÓN
(PX)	CÓDIGO DE PUERTA

ABREVIATURAS	
ÍTEM	DESCRIPCIÓN
N.P.T.	NIVEL DE PISO TERMINADO
N.P.	NIVEL DE PLATAFORMADO
EL.	ELEVACIÓN
S.	PENDIENTE

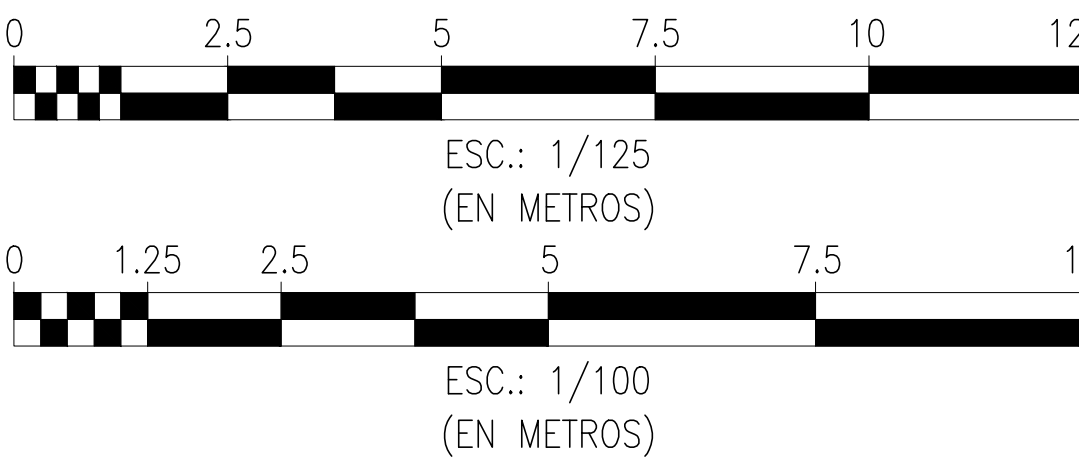

BISA BISA INGENIERÍA DE PROYECTOS S.A.		MINERA CHINALCO PERÚ S.A. CHINALCO	
ESCALA: INDICADA	FORMATO: A1	PROYECTO: INGENIERÍA BÁSICA DE LAS FACILIDADES EN LA NUEVA PLATAFORMA DEL AK-22 FASE II	
DIBUJO: N. QUISPE	FECHA: 11-10-2024	ÁREA: 110	TIPO DE CONTRATO: 1
DISEÑO: L. VERA	FECHA: 11-10-2024	TÍTULO: ÁREA DE LOGÍSTICA	COD.PROYECTO N°: MPDX03
REVISADO: R. QUIÑONEZ	FECHA: 11-10-2024	N° DE PLANO CONTRATISTA: ALMACÉN PATIO-PLANTA DE DISTRIBUCIÓN Y ELEVACIONES	N° DE PLANO: MPDX03-EI23062_66_78-P159CON-110-DW-A-001
APROBADO: C. CARVALLO	FECHA: 11-10-2024		
COD. PROY. CONTRATISTA: DIO39501122	N° DE PLANO CONTRATISTA:		

REFERENCIAS	
-------------	--	--	