
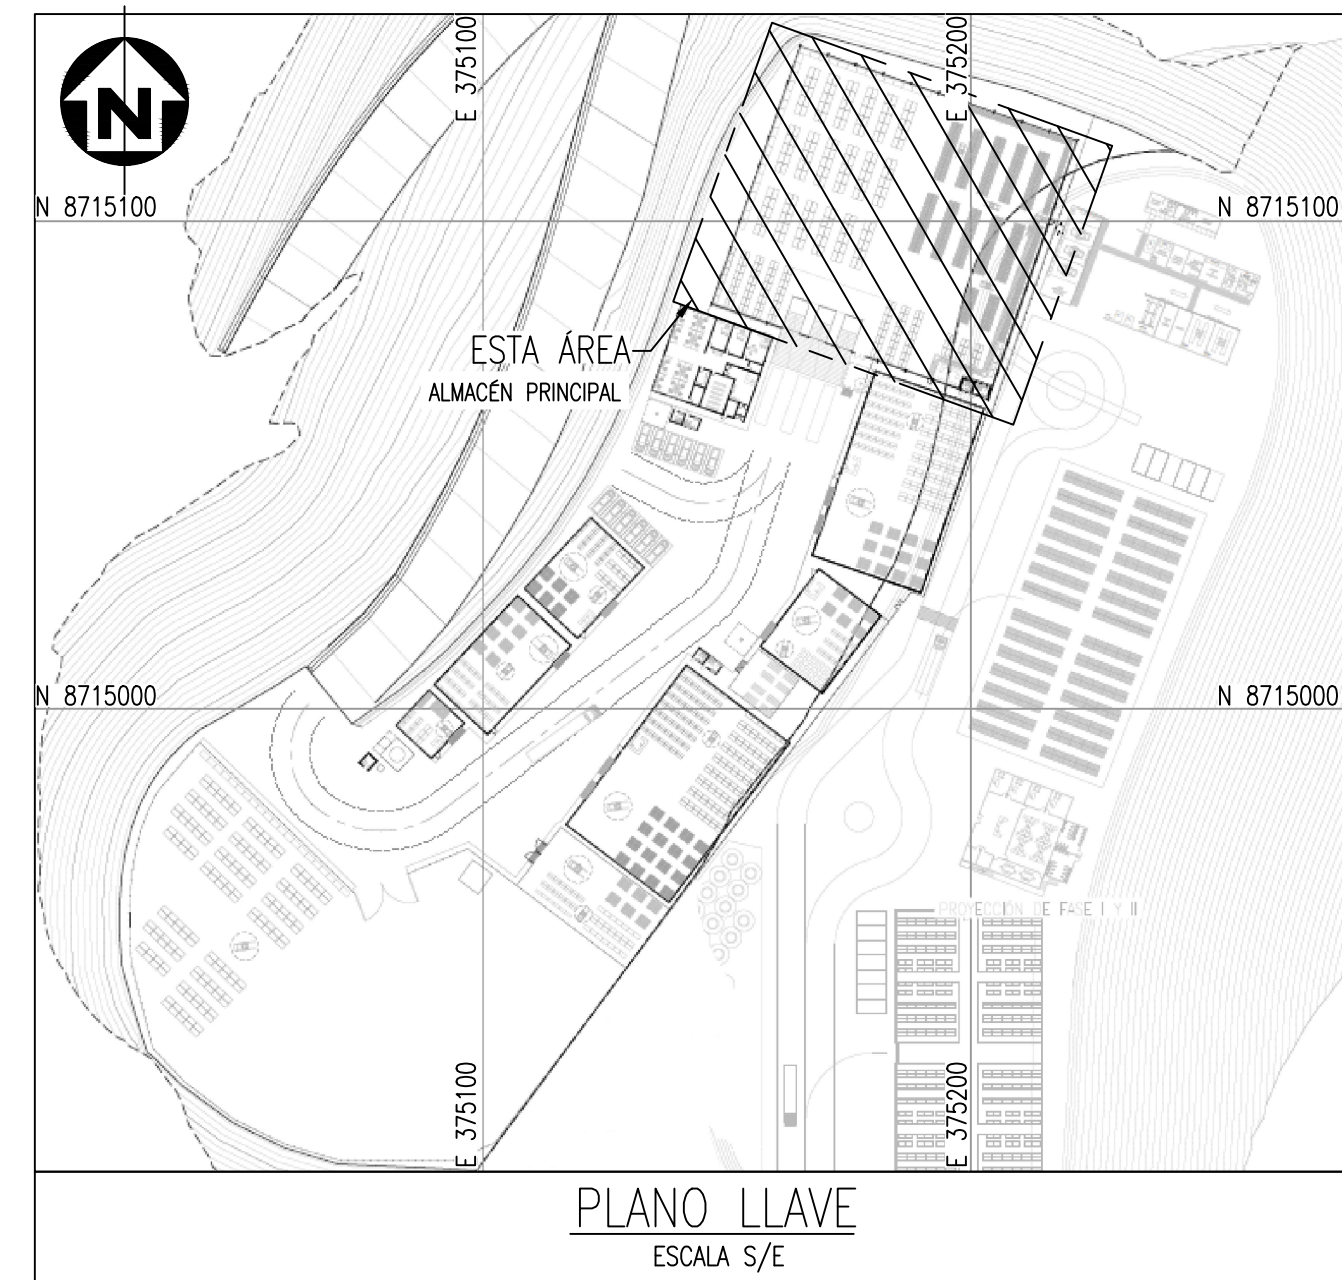


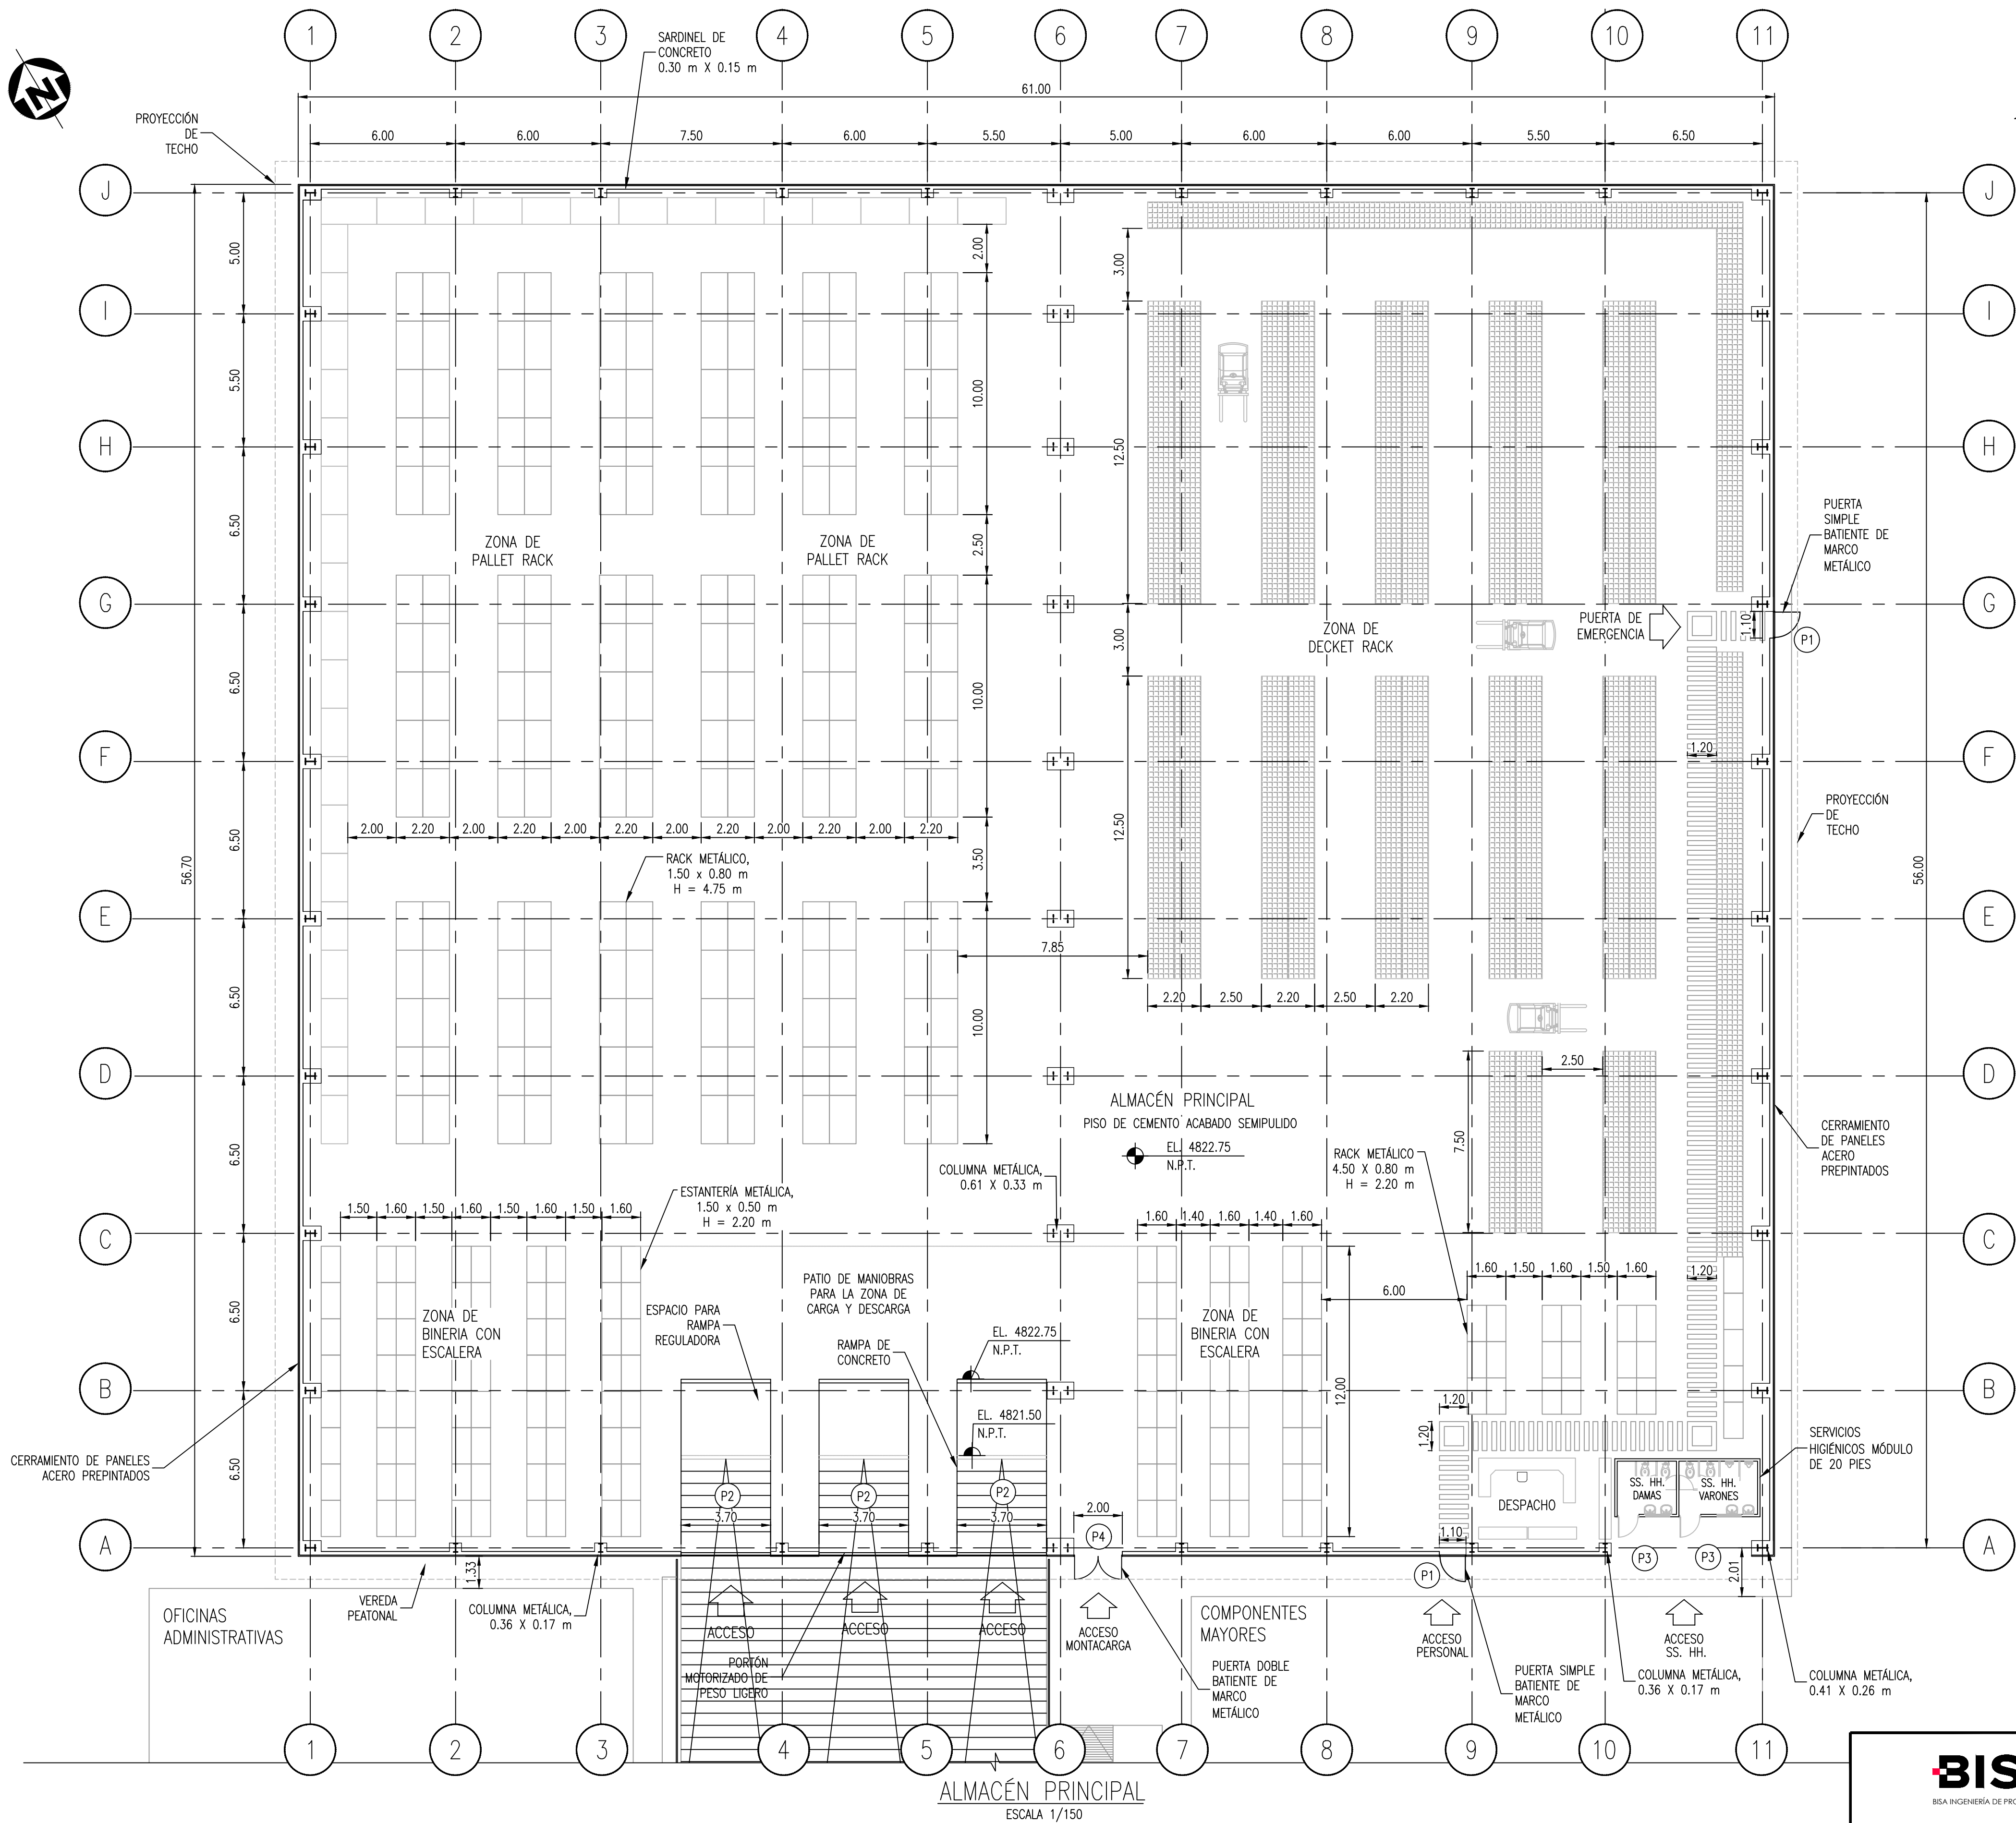


INFORMACIÓN DE LAS EDIFICACIONES				
ÍTEM	COMPONENTE	CANTIDAD	ÁREA TOTAL (m2)	AFORO
1	ALMACÉN PRINCIPAL	1	3360	6 PERS.

CUADRO DE VANOS - PUERTAS						
ÍTEM	SÍMBOLO	ANCHO	ALTO	CANTIDAD	UBICACIÓN	DESCRIPCIÓN
1	(P1)	1.10 m	2.10 m	2	ALMACÉN PRINCIPAL	PUERTA SIMPLE BATIENTE DE MARCO METÁLICO
2	(P2)	3.70 m	5.00 m	3		PORTÓN MOTORIZADO DE PESO LIGERO
3	(P3)	0.90 m	2.10 m	2		PUERTA SIMPLE BATIENTE DE MARCO METÁLICO
4	(P4)	2.00 m	2.10 m	1		PUERTA DOBLE BATIENTE DE MARCO METÁLICO

LEYENDA	
SÍMBOLO	DESCRIPCIÓN
(A)	DESIGNACIÓN DE EJES
EL. XXXX N.P.T.	NIVEL DE PISO TERMINADO
EL. XXXX N.T.T.	NIVEL DE TECHO TERMINADO
EL. XXXX N.P.	NIVEL DE PLATAFORMADO
(PX)	CÓDIGO DE PUERTA

ABREVIATURAS	
SÍMBOLO	DESCRIPCIÓN
N.P.T.	NIVEL DE PISO TERMINADO
N.T.T.	NIVEL DE TECHO TERMINADO
N.P.	NIVEL DE PLATAFORMADO
EL.	ELEVACIÓN
S.	PENDIENTE

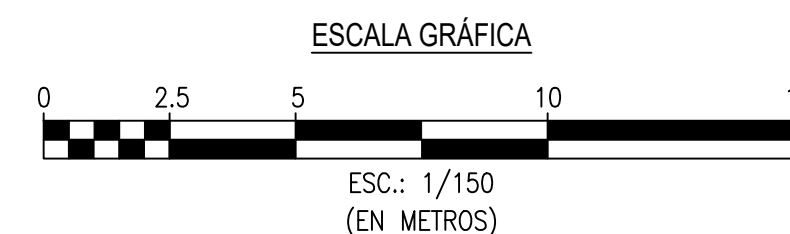

REFERENCIAS	
EI23079-0391_1051-110-DW-C-001	LAYOUT GENERAL - PLANTA
MCP-140-DW-V-019	ALMACÉN PRINCIPAL-PLANTA
MCP-140-DW-V-018	ARREGLO GENERAL-Nv.4822.60-PLANTA
N° DE PLANO/DOCUMENTO	TÍTULO

REVISIONES	
N°	DESCRIPCIÓN
1	EMITIDO PARA USO DEL CLIENTE
2	EMITIDO PARA REVISIÓN DEL CLIENTE
3	EMITIDO PARA REVISIÓN INTERNA
N°	DESCRIPCIÓN

NOTAS:	
1.	TODAS LAS DIMENSIONES SE EXPONEN EN METROS; Y LOS NIVELES, EN MILÍMETROS S.I.C.
2.	TODAS LAS MEDIDAS Y LOS NIVELES DEBERÁN SER VERIFICADOS EN CAMPO EN LA ETAPA DE TRAZO Y REPLANTEO POR EL CONTRATISTA. CUALQUIER INTERFERENCIA O MODIFICACIÓN SE DEBE COORDINAR CON LA SUPERVISIÓN DE MCP.
3.	PARA LA VENTILACIÓN, SE DEBEN CONSIDERAR LOUVERS EN LA SIGUIENTE ETAPA DE INGENIERÍA.
4.	SE DEBE CONSIDERAR 30% DE TRASLÚCIDOS EN LA SIGUIENTE ETAPA DE INGENIERÍA.
5.	ZONA DE BINERÍAS: ESTANTERÍAS DE CARGAS LIGERAS PARA PICKING.

 BISA INGENIERÍA DE PROYECTOS S.A.		 MINERA CHINALCO PERÚ S.A.	
ESCALA: INDICADA		PROYECTO: IMPLEMENTACIÓN NUEVO ALMACÉN TRUCK SHOP LOGÍSTICA AK-22 FASE III	
FORMATO: A1			
DIBUJO: A. GONZÁLEZ	FECHA: 27-03-2024		
DISEÑO: L. VERA	FECHA: 27-03-2024	AREA: 110	TIPO DE CONTRATO:
REVISADO: R. QUIRÓNEZ	FECHA: 27-03-2024		
APROBADO: E.SOTO	FECHA: 27-03-2024	TITULO: ALMACÉN PRINCIPAL	COD.PROYECTO N°: EI23079
COD. PROJ. CONTRATISTA: DIO039501102	N° DE PLANO CONTRATISTA:	PLANTA DE DISTRIBUCIÓN	N° DE PLANO: EI23079-0391_1051-110-DW-A-001