



USUARIO : apezar


ARCHIVO : S:\DIO300\1057D\_Ejecución\03 Planos\02 ESTRUCTURAS\03BANDERA SR-078-03-S016-8500-03-21-0002\_0.dwg

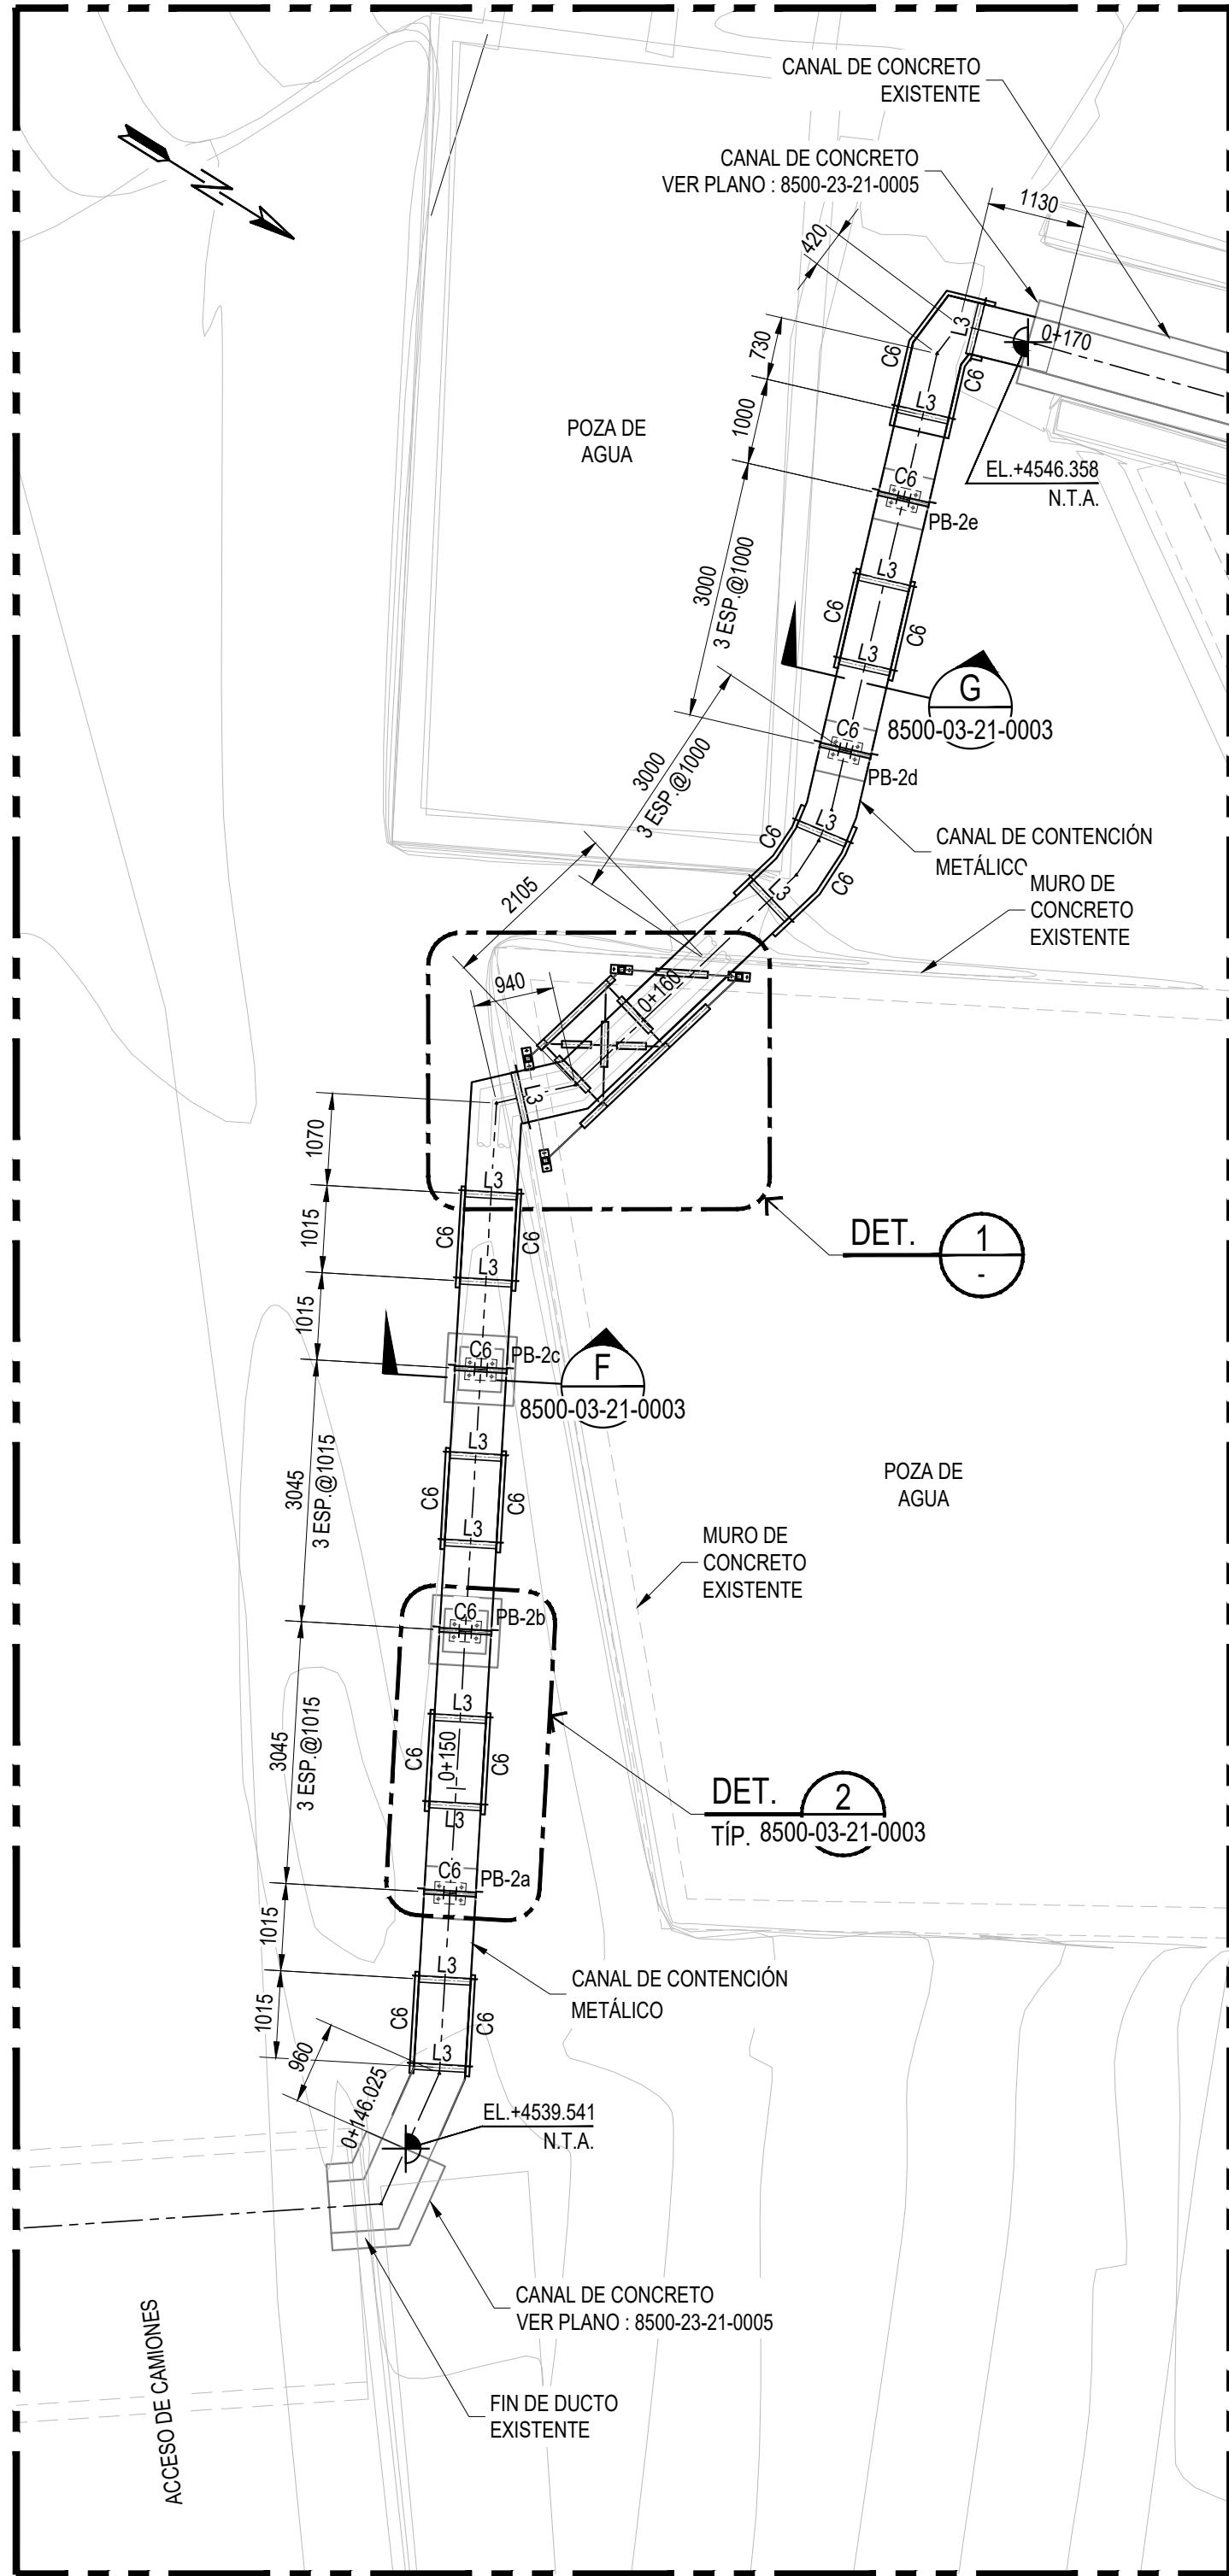

SISTEMA DE CONTENCIÓN LÍNEA 03 - PLANTA (S/C=180 Kg/m<sup>2</sup>)  
PROGRESIVA 0+146.025 A 0+170  
ESC.:1/75

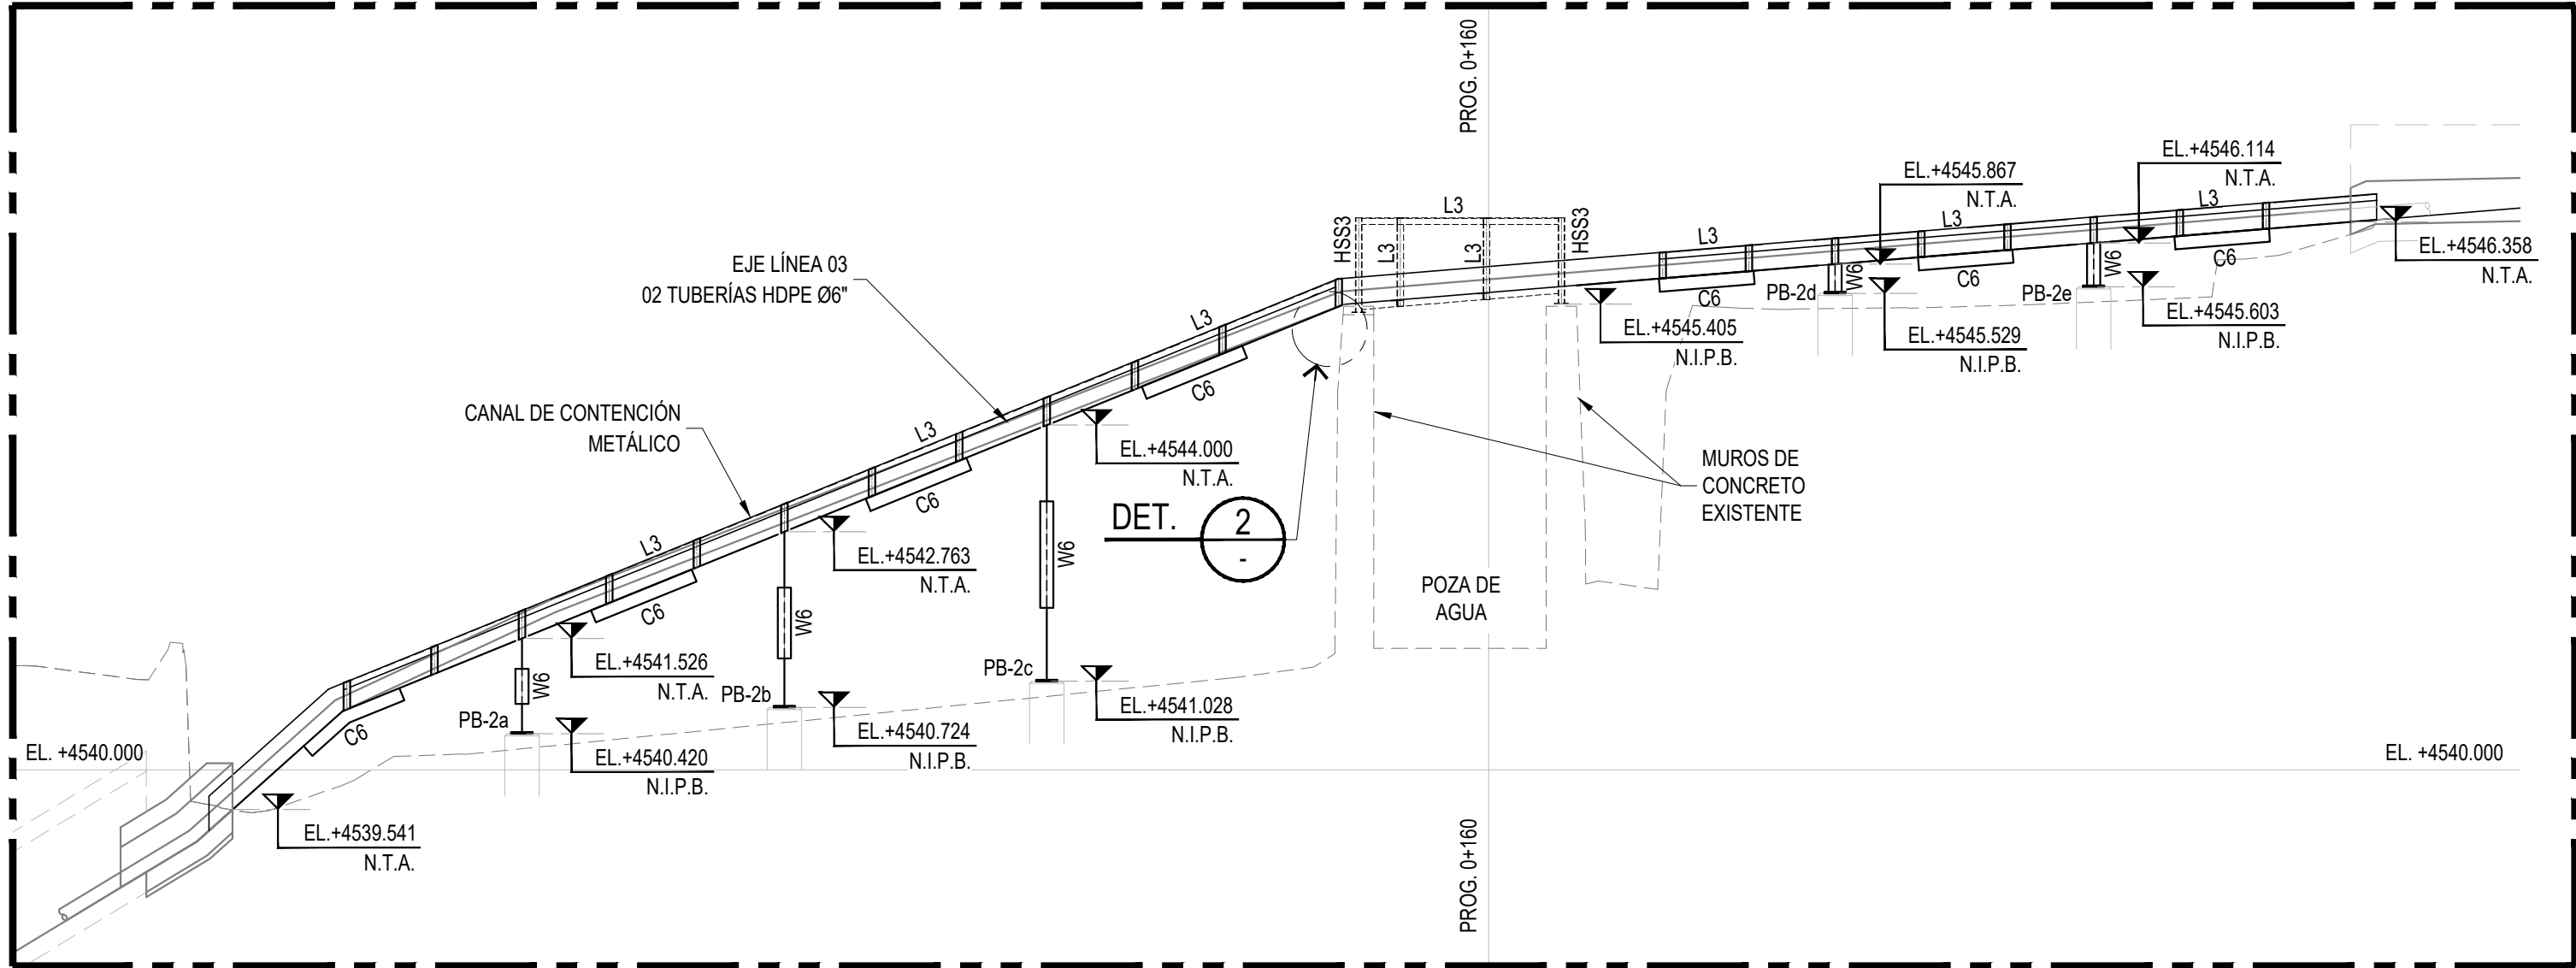


SECCIÓN A-A (VER NOTA 4)  
ESC.:1/75

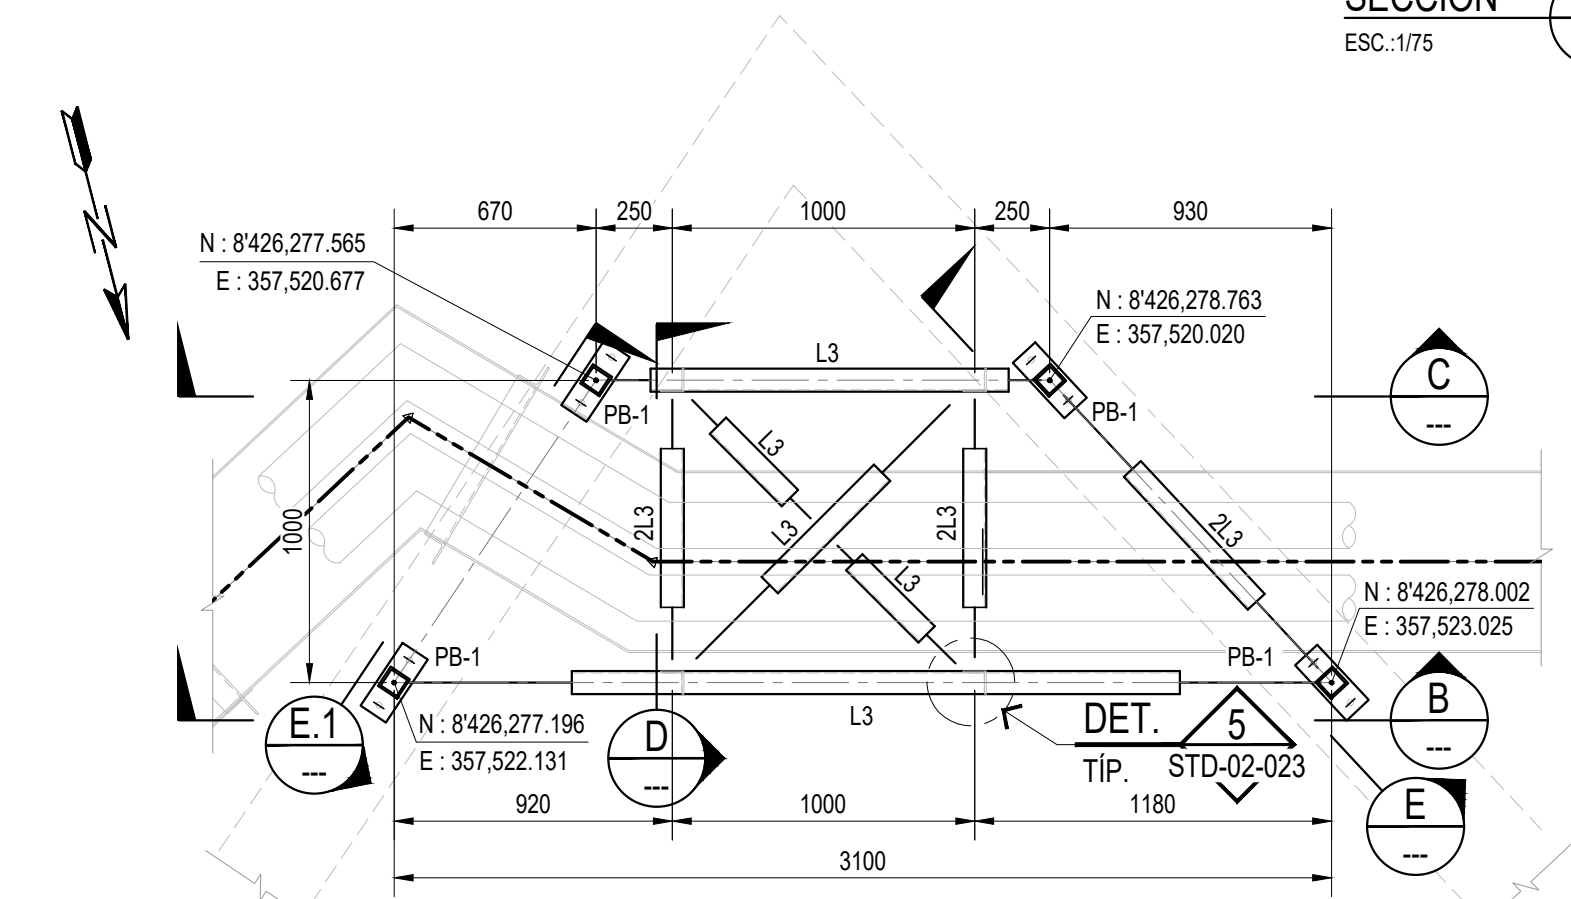


NIVEL N.I.P.B. EL.+4545.380 - PLANTA


DETALLE 1 (VER NOTA 4)  
ESC.:1/25

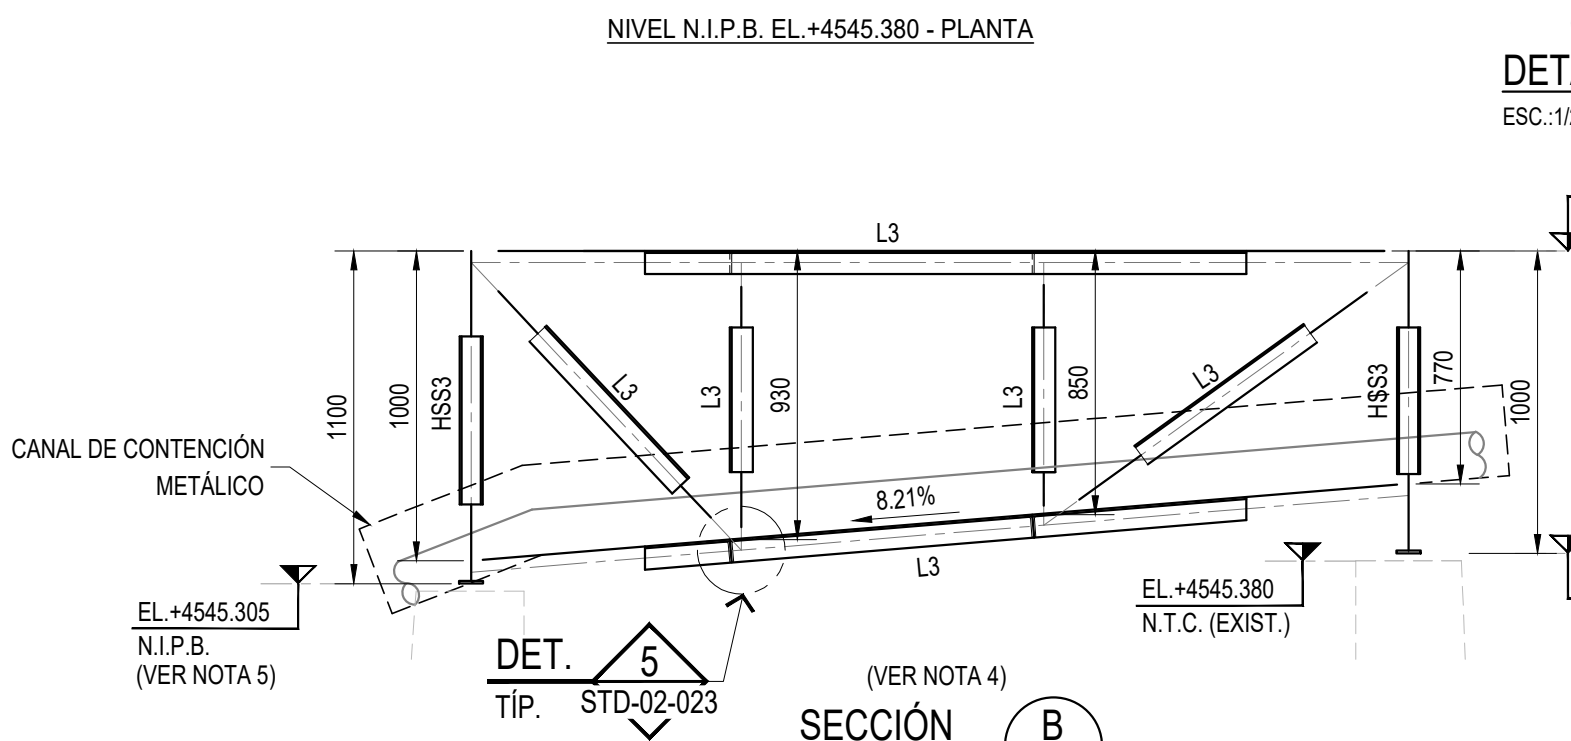


SECCIÓN B-B (VER NOTA 4)  
ESC.:1/25

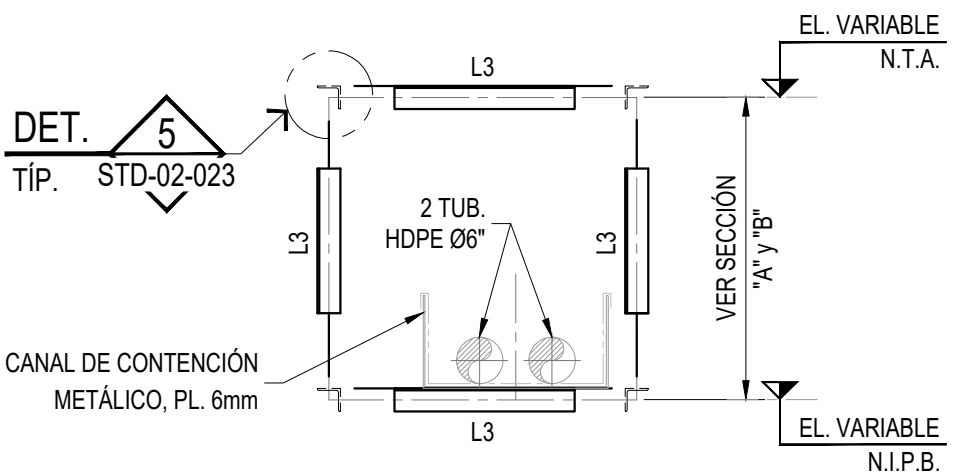


SECCIÓN D-D (VER NOTA 4)  
ESC.:1/25

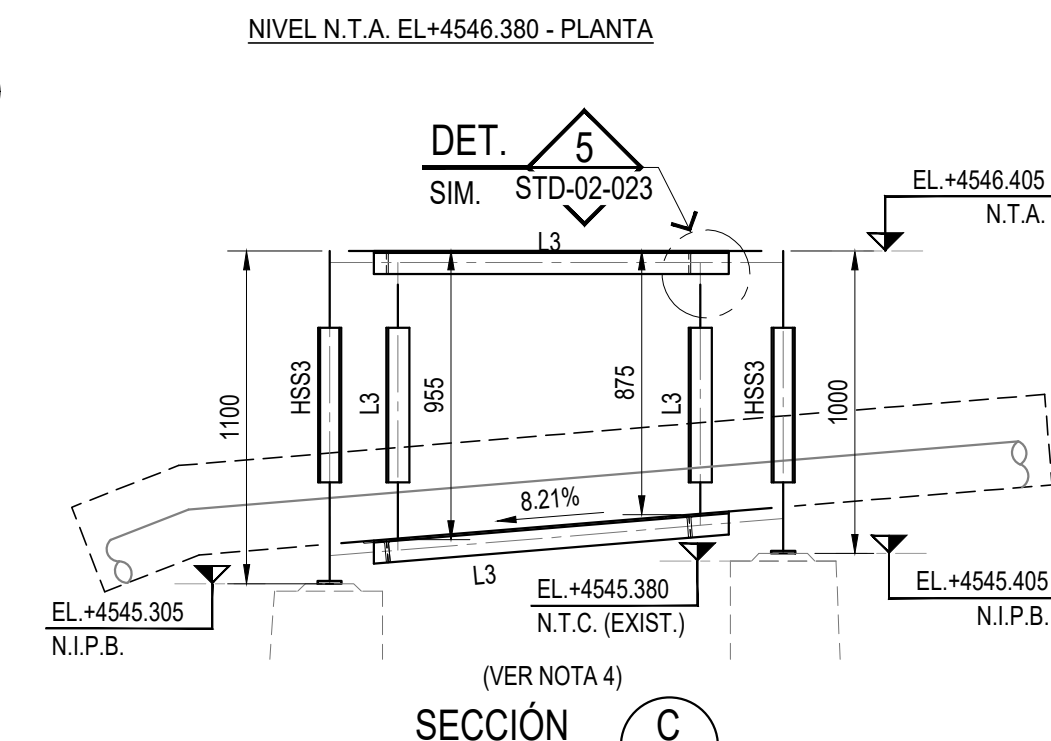

SECCIÓN C-C (VER NOTA 4)  
ESC.:1/25

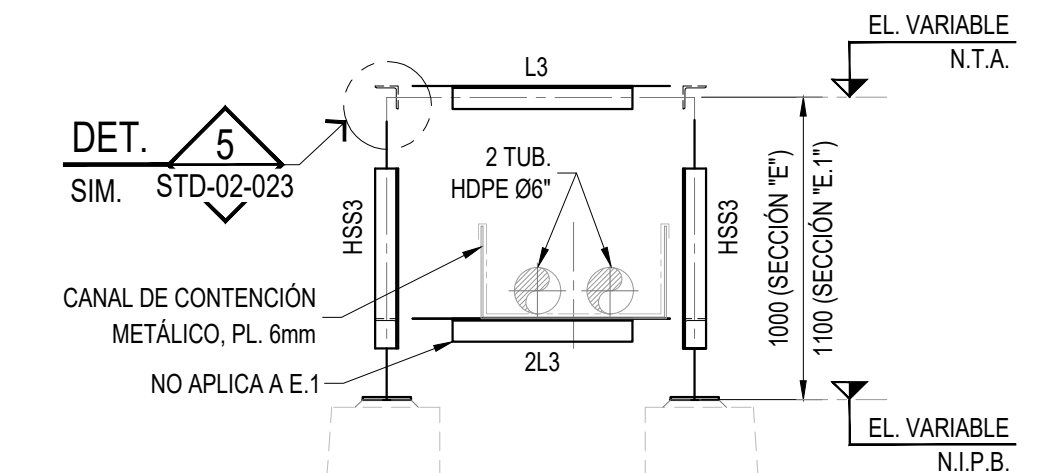

SECCIÓN E-E (VER NOTA 4)  
ESC.:1/25

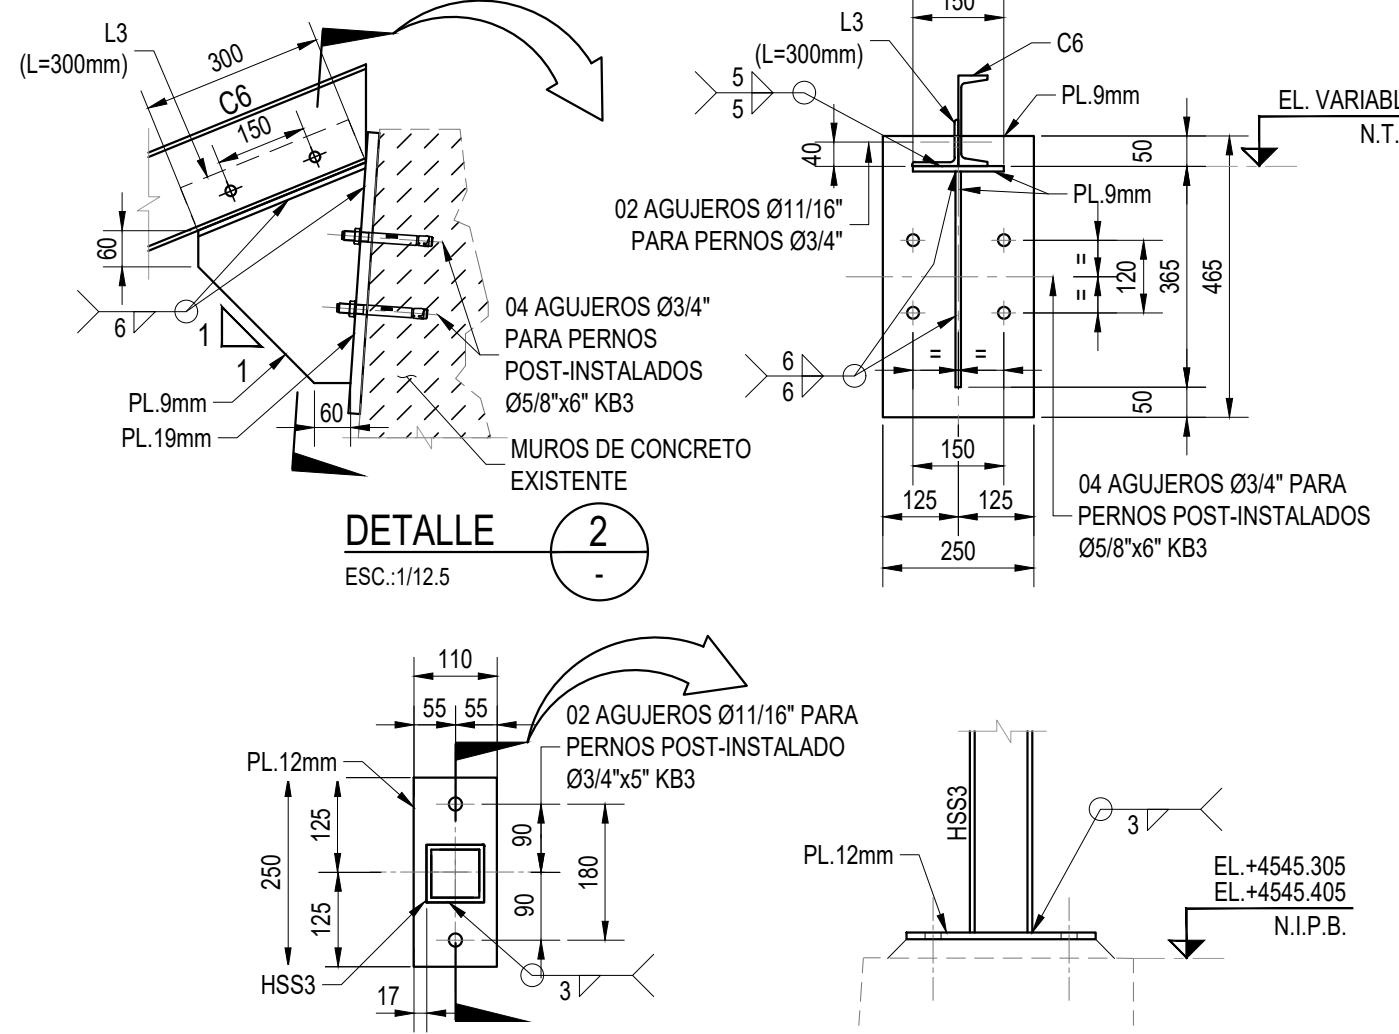

DETALLE DE PLACA BASE PB-1 - PLANTA

### ESPECIFICACIONES TÉCNICAS - ESTRUCTURAS METÁLICAS



- ACERO ESTRUCTURAL:**
- PERFILES LAMINADOS: ASTM A992
  - PERFILES CUADRADOS: ASTM A36
  - PERFILES C, L Y PLATINAS: ASTM A36
- PERNOS DE CONEXIÓN:**
- PARA TODAS LAS CONEXIONES: ASTM A325
  - TUERCAS: ASTM A563 Gr. DH
  - ARANDELAS PLANAS: ASTM F436
  - SOLDADURA: E70XX, AWS-D.1.1 (Fu=70ksi)
- PINTURA**
- VER DOCUMENTO: SR-001-05-0036-0000-03-25-0003

**LEYENDA:**

|      |               |
|------|---------------|
| W6   | : W6x15       |
| C6   | : C6x8.2      |
| L3   | : L3x3x1/4"   |
| 2L3  | : 2L3x3x1/4"  |
| HSS3 | : HSS3x3x1/4" |

**ABREVIATURAS:**

|          |                              |
|----------|------------------------------|
| N.T.A.   | : NIVEL TOPE DE ACERO        |
| N.I.P.B. | : NIVEL INFERIOR PLACA BASE  |
| N.T.C.   | : NIVEL TOPE DE CONCRETO     |
| S.I.C.   | : SALVO INDICACIÓN CONTRARIA |
| TIP.     | : TÍPICO                     |
| EL.      | : ELEVACIÓN                  |
| REF.     | : REFERENCIAL                |
| SIM.     | : SIMILAR                    |

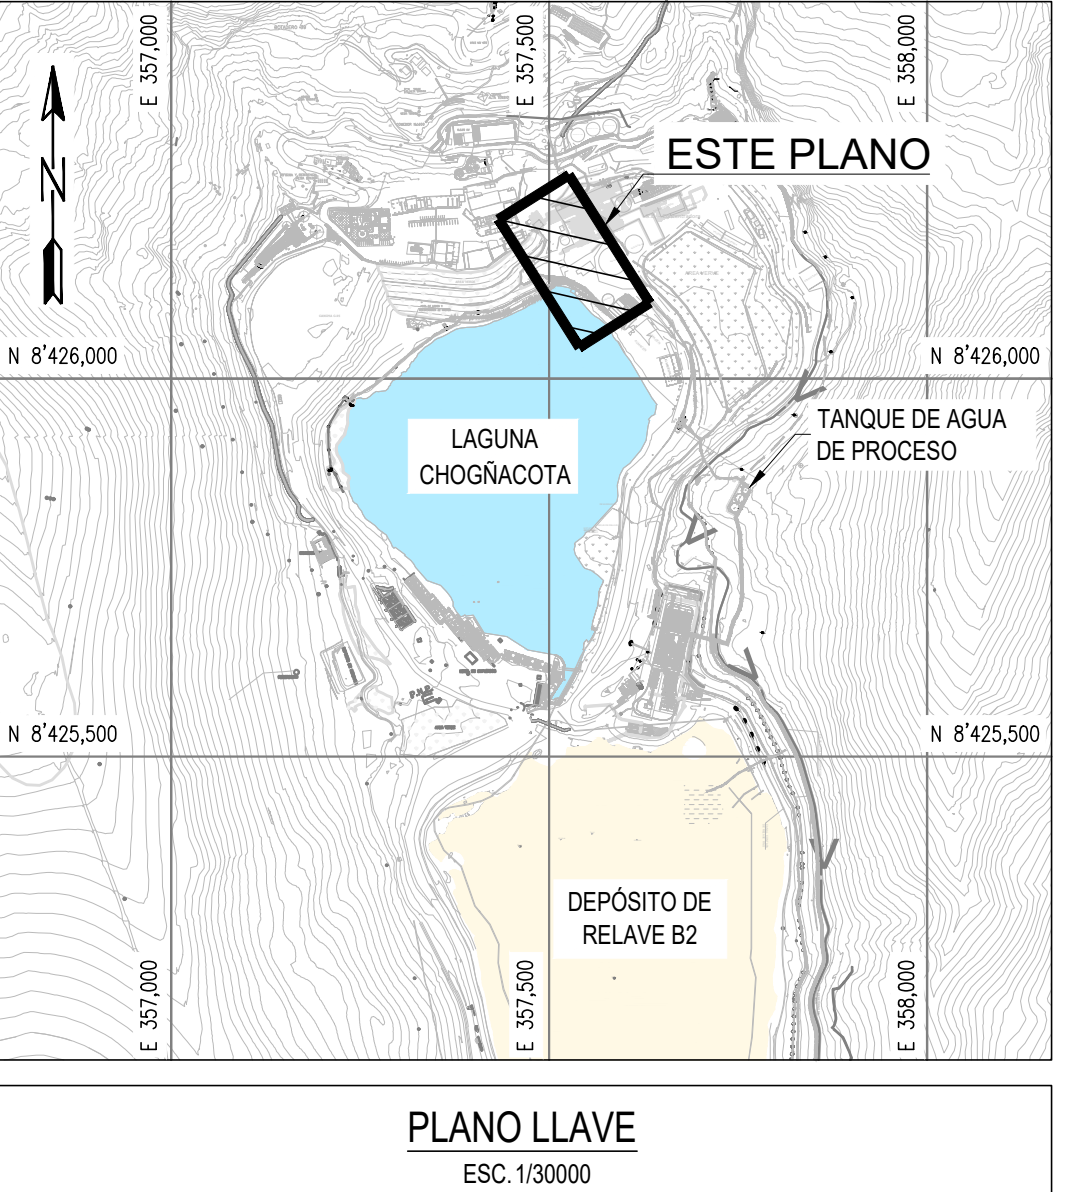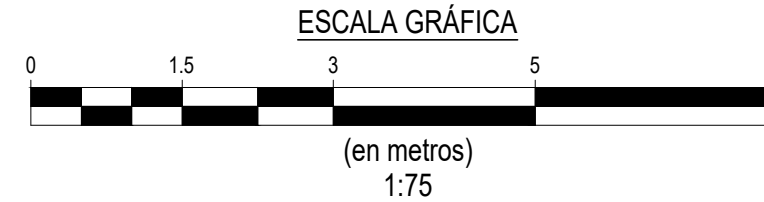

1. LA TOPOGRAFÍA UTILIZADA FUE PROPORCIONADA POR EL CLIENTE Y ESTÁ UBICADA EN EL SISTEMA DE COORDENADAS WGS84, UTM ZONA 19 SUR. VER PLANO DE REFERENCIA: SR-001-MB-L.I.D.L.-OCT-21-001.
2. TODAS LAS DIMENSIONES ESTÁN EN MILÍMETROS, LAS COORDENADAS Y ELEVACIONES ESTÁN EN METROS (S.I.C).
3. TODAS LAS TUBERÍAS SON EXISTENTES Y ESTÁN SOBRE TERRENO.
4. VERIFICAR Y REPLANTEAR UBICACIÓN (COORDENADAS), DIMENSIONES Y NIVELES EN CAMPO. LA INFORMACIÓN DE ESTRUCTURAS EXISTENTES FUERON TOMADAS SEGÚN PLANO PROPORCIONADO POR EL CLIENTE: SR-001-MB-L.I.D.L.-OCT-21-001 y SR-P.M.A.Z.I.-JUL-13-014.
5. NUEVO NIVEL DE MURO EN ZONA A COLOCAR ESTRUCTURA. SE DEMOLERÁ 100mm. VER PLANO: SR-078-03-S016-8500-23-21-0008.

|                 |   |
|-----------------|---|
| 8500-03-21-0003 | LÍNEA 03 - SISTEMA DE CONTENCIÓN PARA LÍNEA 03 (BOMBAS 36F A TANQUES 1200) - CANAL DE CONTENCIÓN METÁLICO - PLANTA, SECCIONES & DETALLES |
| 8500-03-21-0004 | LÍNEA 03 - SISTEMA DE CONTENCIÓN PARA LÍNEA 03 (BOMBAS 36F A TANQUES 1200) - CANAL DE CONTENCIÓN METÁLICO - SECCIÓN                      |
| 8500-23-21-0005 | LÍNEA 03 - SISTEMA DE CONTENCIÓN PARA LÍNEA 03 (BOMBAS 36F A TANQUES 1200) - CANAL DE CONTENCIÓN - PLANTA                                |
| 8500-03-21-0008 | LÍNEA 03 - SISTEMA DE CONTENCIÓN PARA LÍNEA 03 (BOMBAS 36F A TANQUES 1200) - CANAL DE CONTENCIÓN - PLANTA, SECCIONES & DETALLES          |
| 8500-05-21-2007 | CONTENCIÓN DE LÍNEA 3 - TUBERÍAS DE AGUA DE BOMBAS 36F A TANQUES 1200 - ARREGLO GENERAL                                                  |

|          |          |                                                |      |      |      |      |        |
|----------|----------|------------------------------------------------|------|------|------|------|--------|
| 0        | 10-10-22 | EMITIDO PARA CONSTRUCCIÓN                      | A.P. | J.P. | J.G. | E.S. | MINSUR |
| B        | 19-08-22 | EMITIDO PARA REVISIÓN Y APROBACIÓN DEL CLIENTE | A.P. | J.P. | J.G. | E.S. | MINSUR |
| A        | 12-08-22 | EMITIDO PARA REVISIÓN INTERNA                  | A.P. | J.P. | J.G. | E.S. | MINSUR |
| N°. REV. | FECHA    | DESCRIPCIÓN DE LA REVISIÓN                     | DIS. | DIB. | REV. | APR. | CLIENT |

**CONFIDENCIAL**

ESTE PLANO Y LA INFORMACIÓN CONTENIDA SON PROPIEDAD DE BISA INGENIERÍA DE PROYECTOS. SU USO SIN PREVIA AUTORIZACIÓN ESTA PROHIBIDA. CUALQUIER MODIFICACIÓN O ADAPTACIÓN DE LOS DATOS EN EL PLANO SERÁ RESPONSABILIDAD EXCLUSIVA DEL USUARIO SIN NINGUNA RESPONSABILIDAD LEGAL DE BISA.

BISA

BISA INGENIERÍA DE PROYECTOS S.A.

| APROBACIÓN       |             | FECHA          | FIRMA | NOMBRES |               | FECHA       | FIRMA    |          |
|------------------|-------------|----------------|-------|---------|---------------|-------------|----------|----------|
| CLIENTE          | CLIENTE:    |                |       | BISA    | DISEÑADO POR: | A. PÉREZ    | 12-08-22 |          |
|                  | GTE. ING.:  |                |       |         | DIBUJADO POR: | J. PARDAVE  | 12-08-22 |          |
|                  | GTE. PROY.: |                |       |         | REVISADO POR: | J. GONZALEZ | 12-08-22 |          |
|                  |             |                |       |         | APROBADO POR: | E. SOTO     | 12-08-22 |          |
|                  |             |                |       |         | GTE. ING.:    | S. MEZA     | 12-08-22 |          |
| COD. PROY. BISA: |             | PLANO BISA N°: |       |         |               | ESCALA:     |          |          |
| DIO03001057      |             |                |       |         |               |             |          | INDICADA |



minsUR

INGENIERIA DE DETALLE "SISTEMA DE CONTENCIÓN DE FUGAS  
PARA LÍNEAS DE RECUPERACIÓN DE AGUAS Y SIST. DE RELAVES"

LÍNEA 03

SISTEMA DE CONTENCIÓN PARA LÍNEA 03 (BOMBAS 36F A TANQUES 1200)

CANAL DE CONTENCIÓN METÁLICO - PLANTA

COD. PROY. CLIENTE:

PLANO CLIENTE N°:

REV.:

SR-078-03-S016-8500-03-21-0002

0